


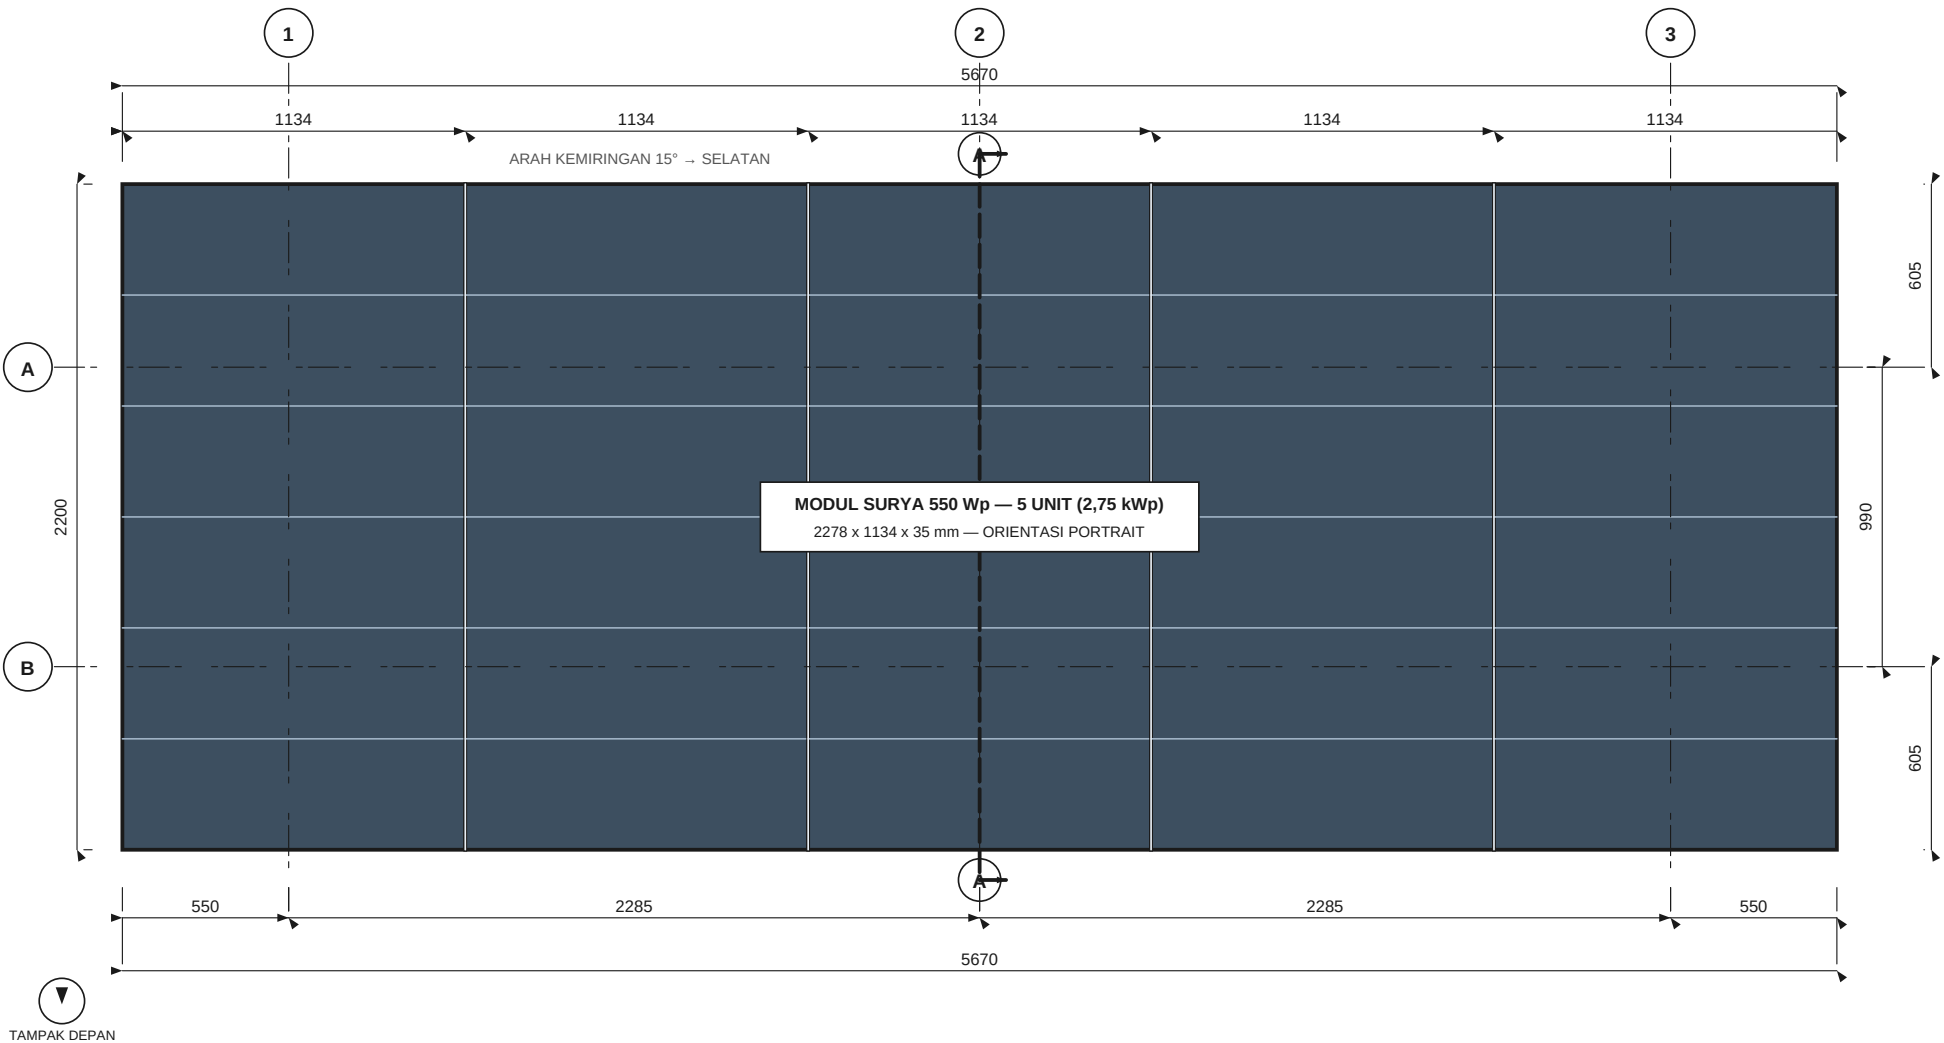

TAMPAK ATAS
SKALA 1 : 25



PANEL MENGHADAP UTARA
(azimuth 0° — sesuaikan site)

CATATAN :

- Semua ukuran dalam milimeter (mm), elevasi dalam meter dari ±0.00 lantai kerja. Gambar menyempurnakan draft awal; dimensi antar tampak telah diserasikan.
- Modul surya 550 Wp sebanyak 5 unit (total 2,75 kWp), dipasang portrait, kemiringan 15 derajat menghadap UTARA (sesuaikan azimuth dengan lokasi site).
- Rangka seluruhnya baja hollow galvanis 40 x 20 mm (tebal min. 1,6 mm). Semua sambungan rangka DILAS dan diperiksa kerataannya.
- Kaki rangka diangkur ke sloof melalui plat besi 5 mm (100 x 100 mm) dengan 4 dynabolt M12 per titik. Pastikan plat rata & level (toleransi ±5 mm).
- Sloof & balok ikat beton mutu K-225, tulangan Ø8 mm, besi cincin (sengkang) jarak 15 cm. Semua struktur beton dituang monolit (disatukan).
- Pondasi batu kali 6 titik: lebar atas 30 cm, bawah 60 cm, kedalaman 50 cm di bawah sloof. Lantai kerja beton tebal 10 cm di sekeliling struktur.
- Jarak antar rangka (sumbu 1-2-3) 2285 mm; kantilever rail di ujung 550 mm. Rail memanjang 2 jalur di atas baris kaki.
- Pembumian (grounding) rangka & modul serta instalasi kabel DC mengikuti PUIL 2011 dan petunjuk pabrikan modul.

LEGENDA :

- Tepi benda terlihat
- Tepi benda tersembunyi
- Garis dimensi / leader
- Garis sumbu
- Arsir beton / detail tipis
- Kotak gelap : modul surya
- Tanah asli


DAFTAR LEMBAR GAMBAR :

G-01	TAMPAK ATAS
G-02	TAMPAK DEPAN
G-03	TAMPAK SAMPIING (POTONGAN A-A)
G-04	TAMPAK ATAS - PANEL SURYA DISAMARKAN (RANGKA)
G-05	TAMPAK ATAS - PANEL DIHILANGKAN (RANGKA & BETON)
G-06	TAMPAK ATAS - PANEL & RANGKA DISAMARKAN (BETON)

DAFTAR KEBUTUHAN MATERIAL (BOM) :

NO	URAIAN MATERIAL	SPESIFIKASI	SAT.	QTY	
1	Modul surya 550 Wp	2278 x 1134 x 35 mm	unit	5	
2	Baja hollow galvanis 40 x 20 x 1,6 mm — balk rail memanjang	2 x 5,67 m	m	11,34	
3	Baja hollow galvanis 40 x 20 x 1,6 mm — kaki rangka	3 x 1,09 m + 3 x 1,36 m	m	7,35	
4	Baja hollow galvanis 40 x 20 x 1,6 mm — pengaku & braket box	6 x 1,34 m + braket	m	5,30	
5	Klem modul (tengah & ujung) + baut M8	sesuai pabrikan modul	set	24	
6	Plat besi alas kaki	5 mm, 100 x 100 mm	pcs	6	
7	Dynabolt / angkur ekspansi	M12 x 100 mm (4 bh/titik)	pcs	24	
8	Beton sloof & balok ikat	mutu K-225	m3	1,05	
9	Pondasi batu kali (1 : 5)	atas 30, bawah 60, dalam 50 cm	titik	6	
10	Beton lantai kerja	K-100, tebal 10 cm	m3	2,00	
11	Besi beton polos Ø8	tulangan + sengkang @15 cm	kg	50	
12	Box panel control + dudukan	IP65, sesuai spesifikasi	unit	1	

DIGAMBAR	DIPERIKSA	DISAHKAN			
NAMA / TGL :	NAMA / TGL :	NAMA / TGL :			
PEMBANGUNAN PLTS GROUND MOUNT 2,75 kWp					
LOKASI / PEKERJAAN : (diisi sesuai lokasi proyek)					
JUDUL GAMBAR : TAMPAK ATAS — RENCANA SUSUNAN MODUL					
NO. GAMBAR	SKALA	SAT.	TANGGAL	REVISI	STATUS
G-01	1 : 25	mm	18-09-2026	0	KONSTRUKSI

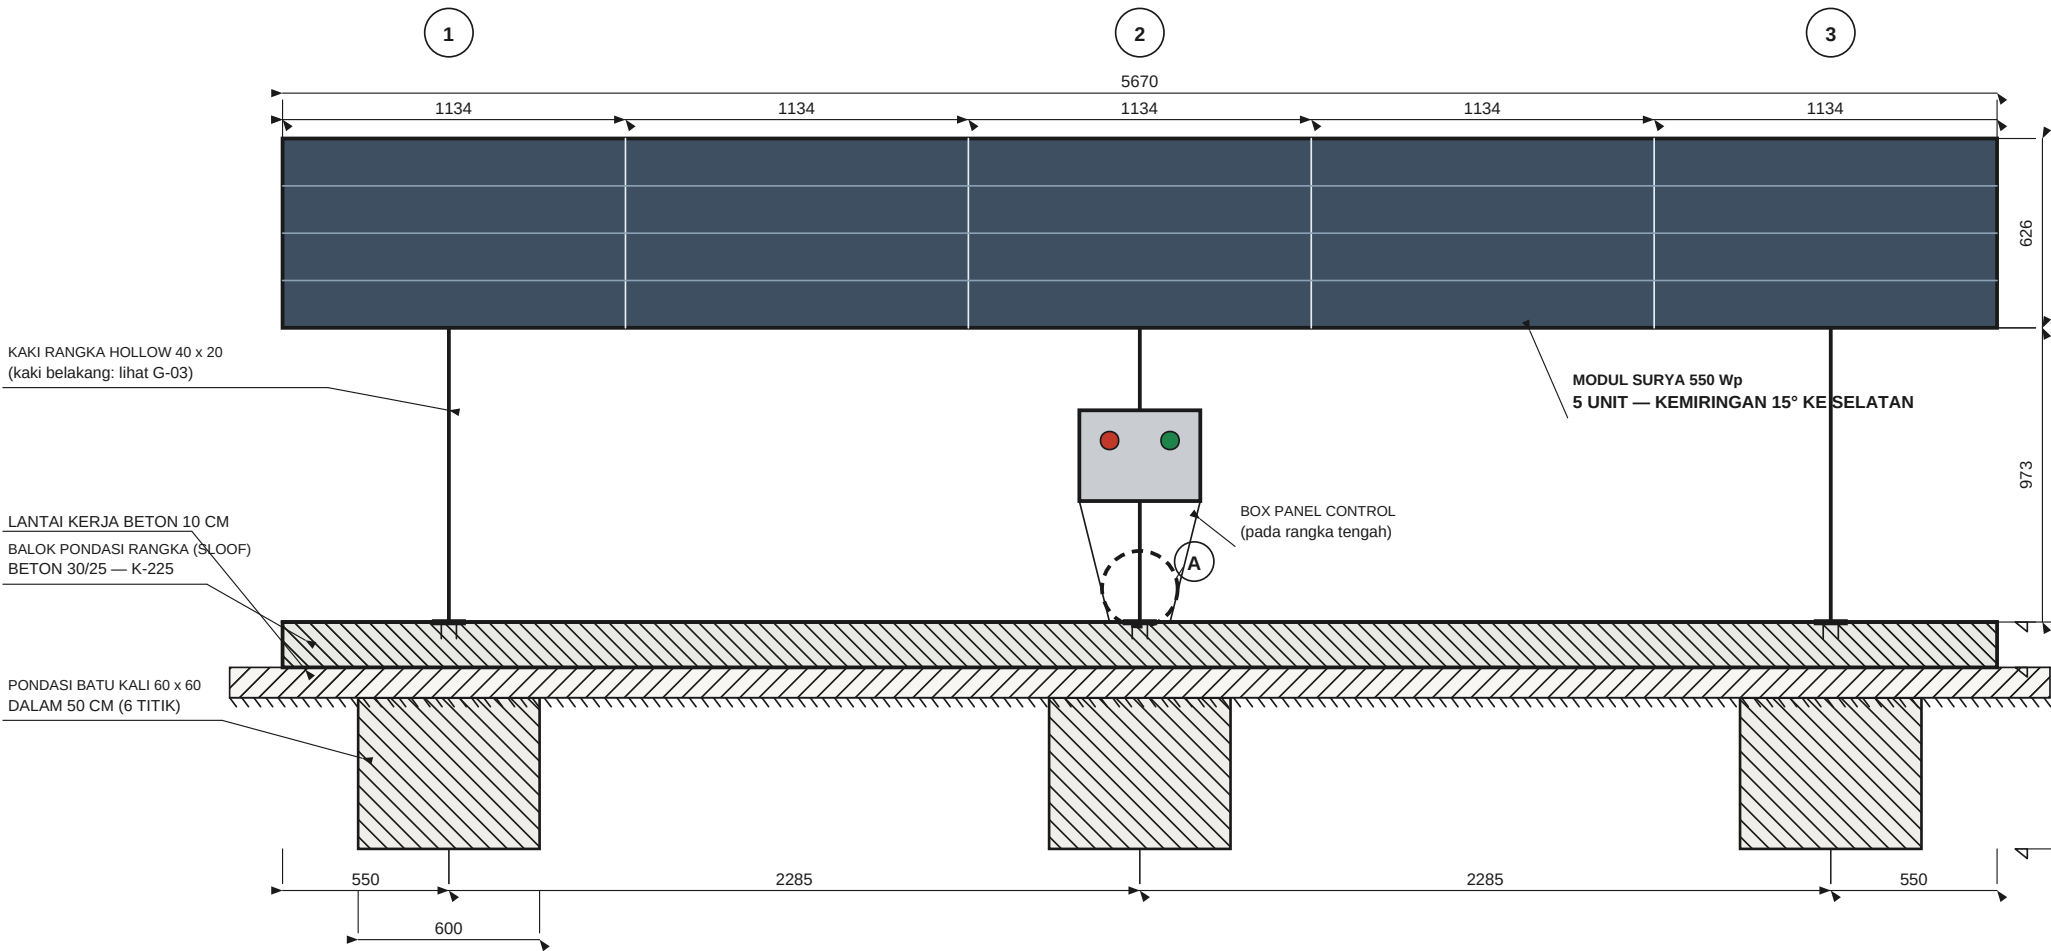


TAMPAK DEPAN

SKALA 1 : 25

DIPANDAT DARI ARAH UTARA (KE SELATAN)

DETAIL A — SAMBUNGAN KAKI RANGKA

SKALA 1 : 5

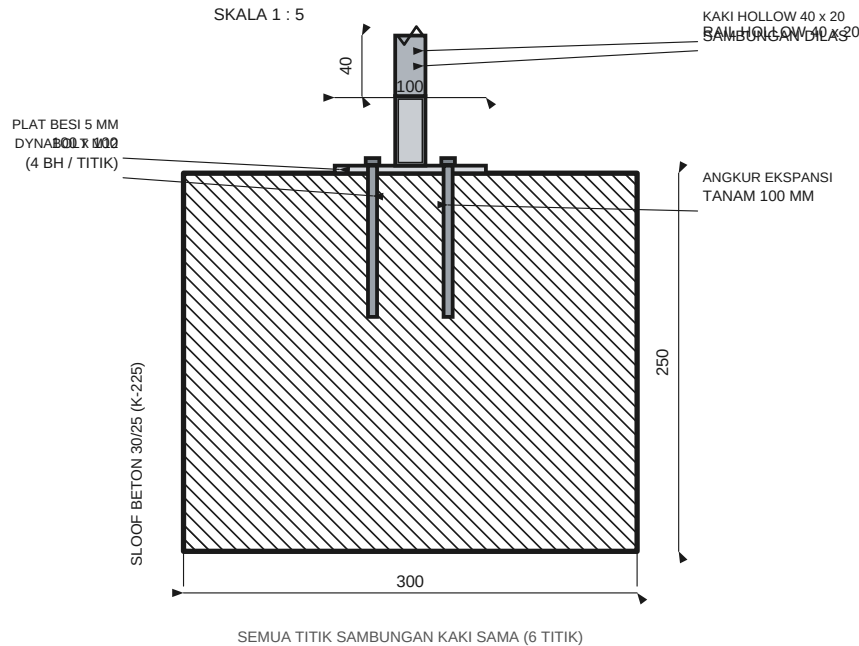

CATATAN :

- Semua ukuran dalam milimeter (mm), elevasi dalam meter dari ±0.00 lantai kerja. Gambar menyempurnakan draft awal; dimensi antar tampak telah diserasikan.
- Modul surya 550 Wp sebanyak 5 unit (total 2,75 kWp), dipasang portrait, kemiringan 15 derajat menghadap UTARA (sesuaikan azimuth dengan lokasi site).
- Rangka seluruhnya baja hollow galvanis 40 x 20 mm (tebal min. 1,6 mm). Semua sambungan rangka DILAS dan diperiksa kerataannya.
- Kaki rangka diangkur ke sloof melalui plat besi 5 mm (100 x 100 mm) dengan 4 dynabolt M12 per titik. Pastikan plat rata & level (toleransi ±5 mm).
- Sloof & balok ikat beton mutu K-225, tulangan Ø8 mm, besi cincin (senggang) jarak 15 cm. Semua struktur beton dituang monolit (disatukan).
- Pondasi batu kali 6 titik: lebar atas 30 cm, bawah 60 cm, kedalaman 50 cm di bawah sloof. Lantai kerja beton tebal 10 cm di sekeliling struktur.
- Jarak antar rangka (sumbu 1-2-3) 2285 mm; kantilever rail di ujung 550 mm. Rail memanjang 2 jalur di atas baris kaki.
- Pembumian (grounding) rangka & modul serta instalasi kabel DC mengikuti PUIL 2011 dan petunjuk pabrikan modul.


LEGENDA :

- Tepi benda terlihat
- Tepi benda tersembunyi
- Garis dimensi / leader
- Garis sumbu
- Arsir beton / detail tipis
- Kotak gelap : modul surya
- Tanah asli

DAFTAR LEMBAR GAMBAR :

G-01	TAMPAK ATAS
G-02	TAMPAK DEPAN
G-03	TAMPAK SAMPING (POTONGAN A-A)
G-04	TAMPAK ATAS - PANEL SURYA DISAMARKAN (RANGKA)
G-05	TAMPAK ATAS - PANEL DIHILANGKAN (RANGKA & BETON)
G-06	TAMPAK ATAS - PANEL & RANGKA DISAMARKAN (BETON)

DIGAMBAR	DIPERIKSA	DISAHKAN			
NAMA / TGL :	NAMA / TGL :	NAMA / TGL :			
PEMBANGUNAN PLTS GROUND MOUNT 2,75 kWp					
LOKASI / PEKERJAAN : (diisi sesuai lokasi proyek)					
JUDUL GAMBAR : TAMPAK DEPAN — ELEVASI DARI ARAH UTARA					
NO. GAMBAR	SKALA	SAT.	TANGGAL	REVISI	STATUS
G-02	1 : 25	mm	18-09-2026	0	KONSTRUKSI

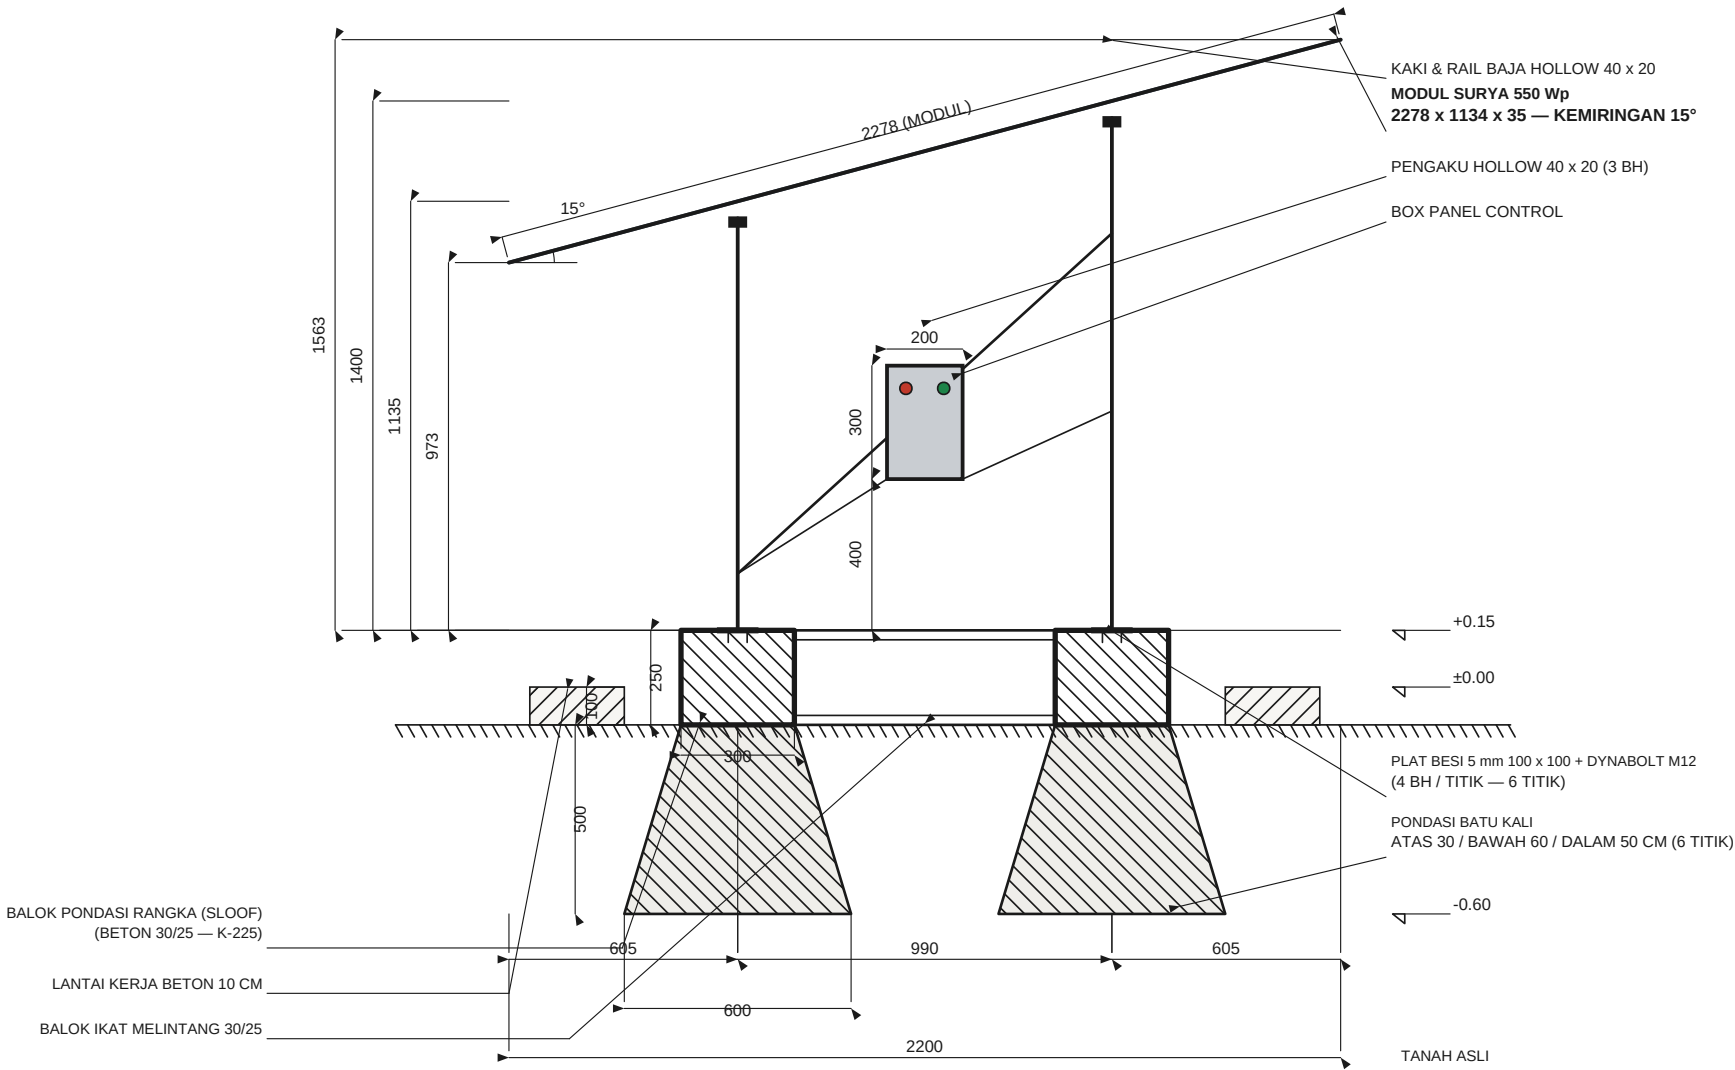

TAMPAK SAMPING (POTONGAN A-A)

SKALA 1 : 20

POTONGAN PADA SUMBU 2 — DIPANDANG DARI BARAT (KE TIMUR)

CATATAN :

- Semua ukuran dalam milimeter (mm), elevasi dalam meter dari ±0.00 lantai kerja. Gambar menyempurnakan draft awal; dimensi antar tampak telah disesuaikan.
- Modul surya 550 Wp sebanyak 5 unit (total 2,75 kWp), dipasang portrait, kemiringan 15 derajat menghadap UTARA (sesuaikan azimuth dengan lokasi site).
- Rangka seluruhnya baja hollow galvanis 40 x 20 mm (tebal min. 1,6 mm). Semua sambungan rangka DILAS dan diperiksa kerataannya.
- Kaki rangka diangkur ke sloof melalui plat besi 5 mm (100 x 100 mm) dengan 4 dynabolt M12 per titik. Pastikan plat rata & level (toleransi ±5 mm).
- Sloof & balok ikat beton mutu K-225, tulangan Ø8 mm, besi cincin (sengkang) jarak 15 cm. Semua struktur beton dituang monolit (disatukan).
- Pondasi batu kali 6 titik: lebar atas 30 cm, bawah 60 cm, kedalaman 50 cm di bawah sloof. Lantai kerja beton tebal 10 cm di sekeliling struktur.
- Jarak antar rangka (sumbu 1-2-3) 2285 mm; kantilever rail di ujung 550 mm. Rail memanjang 2 jalur di atas baris kaki.
- Pembumian (grounding) rangka & modul serta instalasi kabel DC mengikuti PUIL 2011 dan petunjuk pabrikan modul.


LEGENDA :

- Tepi benda terlihat
- Tepi benda tersembunyi
- Garis dimensi / leader
- Garis sumbu
- Arsir beton / detail tipis
- Kotak gelap : modul surya
- Tanah asli

DAFTAR LEMBAR GAMBAR :

G-01	TAMPAK ATAS
G-02	TAMPAK DEPAN
G-03	TAMPAK SAMPING (POTONGAN A-A)
G-04	TAMPAK ATAS - PANEL SURYA DISAMARKAN (RANGKA)
G-05	TAMPAK ATAS - PANEL DIHILANGKAN (RANGKA & BETON)
G-06	TAMPAK ATAS - PANEL & RANGKA DISAMARKAN (BETON)

DIGAMBAR	DIPERIKSA	DISAHKAN			
_____	_____	_____			
NAMA / TGL :	NAMA / TGL :	NAMA / TGL :			
PEMBANGUNAN PLTS GROUND MOUNT 2,75 kWp					
LOKASI / PEKERJAAN : (diisi sesuai lokasi proyek)					
JUDUL GAMBAR : TAMPAK SAMPING — POTONGAN A-A (SUMBU 2)					
NO. GAMBAR	SKALA	SAT.	TANGGAL	REVISI	STATUS
G-03	1 : 20	mm	18-09-2026	0	KONSTRUKSI

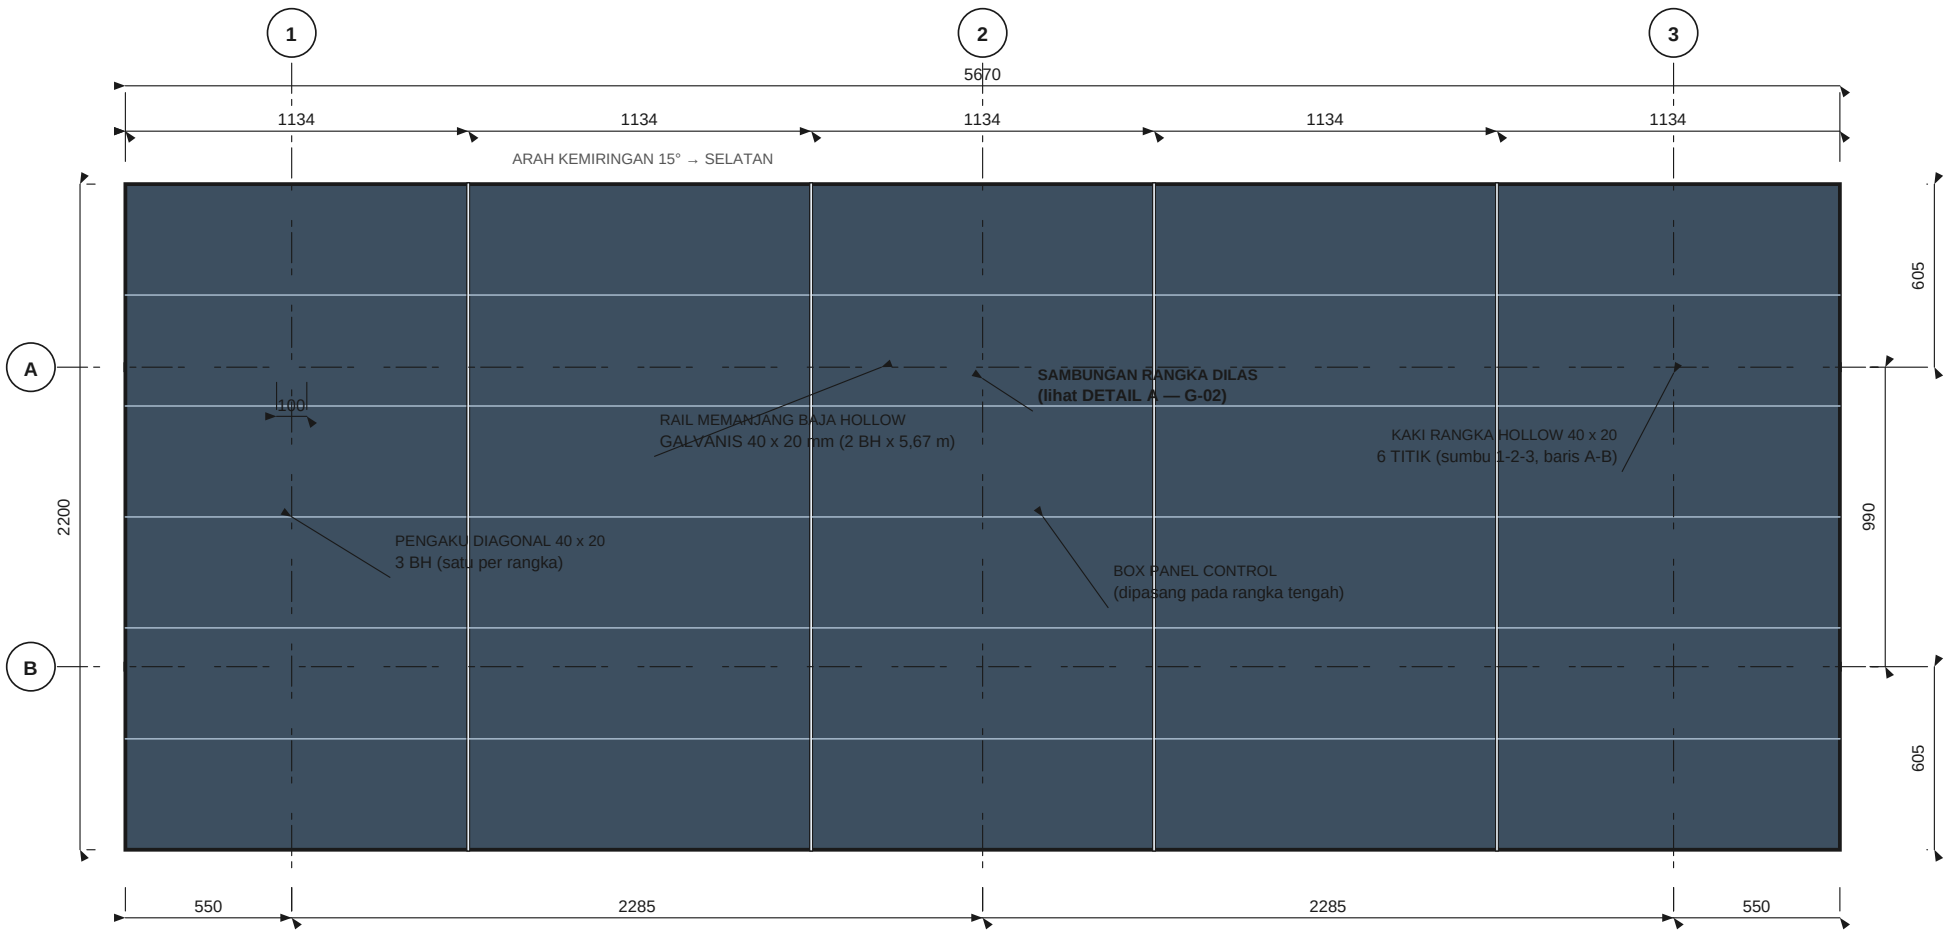

CATATAN :

- Semua ukuran dalam milimeter (mm), elevasi dalam meter dari ±0.00 lantai kerja. Gambar menyempurnakan draft awal; dimensi antar tampak telah diserasikan.
- Modul surya 550 Wp sebanyak 5 unit (total 2,75 kWp), dipasang portrait, kemiringan 15 derajat menghadap UTARA (sesuaikan azimuth dengan lokasi site).
- Rangka seluruhnya baja hollow galvanis 40 x 20 mm (tebal min. 1,6 mm). Semua sambungan rangka DILAS dan diperiksa kerataannya.
- Kaki rangka diangkur ke sloof melalui plat besi 5 mm (100 x 100 mm) dengan 4 dynabolt M12 per titik. Pastikan plat rata & level (toleransi ±5 mm).
- Sloof & balok ikat beton mutu K-225, tulangan Ø8 mm, besi cincin (sengkang) jarak 15 cm. Semua struktur beton dituang monolit (disatukan).
- Pondasi batu kali 6 titik: lebar atas 30 cm, bawah 60 cm, kedalaman 50 cm di bawah sloof. Lantai kerja beton tebal 10 cm di sekeliling struktur.
- Jarak antar rangka (sumbu 1-2-3) 2285 mm; kantilever rail di ujung 550 mm. Rail memanjang 2 jalur di atas baris kaki.
- Pembumian (grounding) rangka & modul serta instalasi kabel DC mengikuti PUIL 2011 dan petunjuk pabrikan modul.

LEGENDA :

- Tepi benda terlihat
- Tepi benda tersembunyi
- Garis dimensi / leader
- Garis sumbu
- Arsir beton / detail tipis
- Kotak gelap : modul surya
- Tanah asli


TAMPAK ATAS — RANGKA PANEL

SKALA 1 : 25

DAFTAR BATANG RANGKA :

KODE	URAIAN	PENAMPANG	JML	PANJANG	
K-1	Kaki depan (baris A)	Hollow 40 x 20	3	1.090 m	
K-2	Kaki belakang (baris B)	Hollow 40 x 20	3	1.355 m	
R-1	Rail memanjang	Hollow 40 x 20	2	5.670 m	
P-1	Pengaku diagonal	Hollow 40 x 20	3	1.340 m	
P-2	Braket dudukan box	Hollow 40 x 20	2	0.350 m	
PL-1	Plat besi alas kaki	Plat 5 mm, 100 x 100	6	—	

DIGAMBAR		DIPERIKSA		DISAHKAN	
_____		_____		_____	
NAMA / TGL :		NAMA / TGL :		NAMA / TGL :	
PEMBANGUNAN PLTS GROUND MOUNT 2,75 kWp					
LOKASI / PEKERJAAN : (diisi sesuai lokasi proyek)					
JUDUL GAMBAR : TAMPAK ATAS — RANGKA PANEL (PANEL DISAMARKAN)					
NO. GAMBAR	SKALA	SAT.	TANGGAL	REVISI	STATUS
G-04	1 : 25	mm	18-09-2026	0	KONSTRUKSI

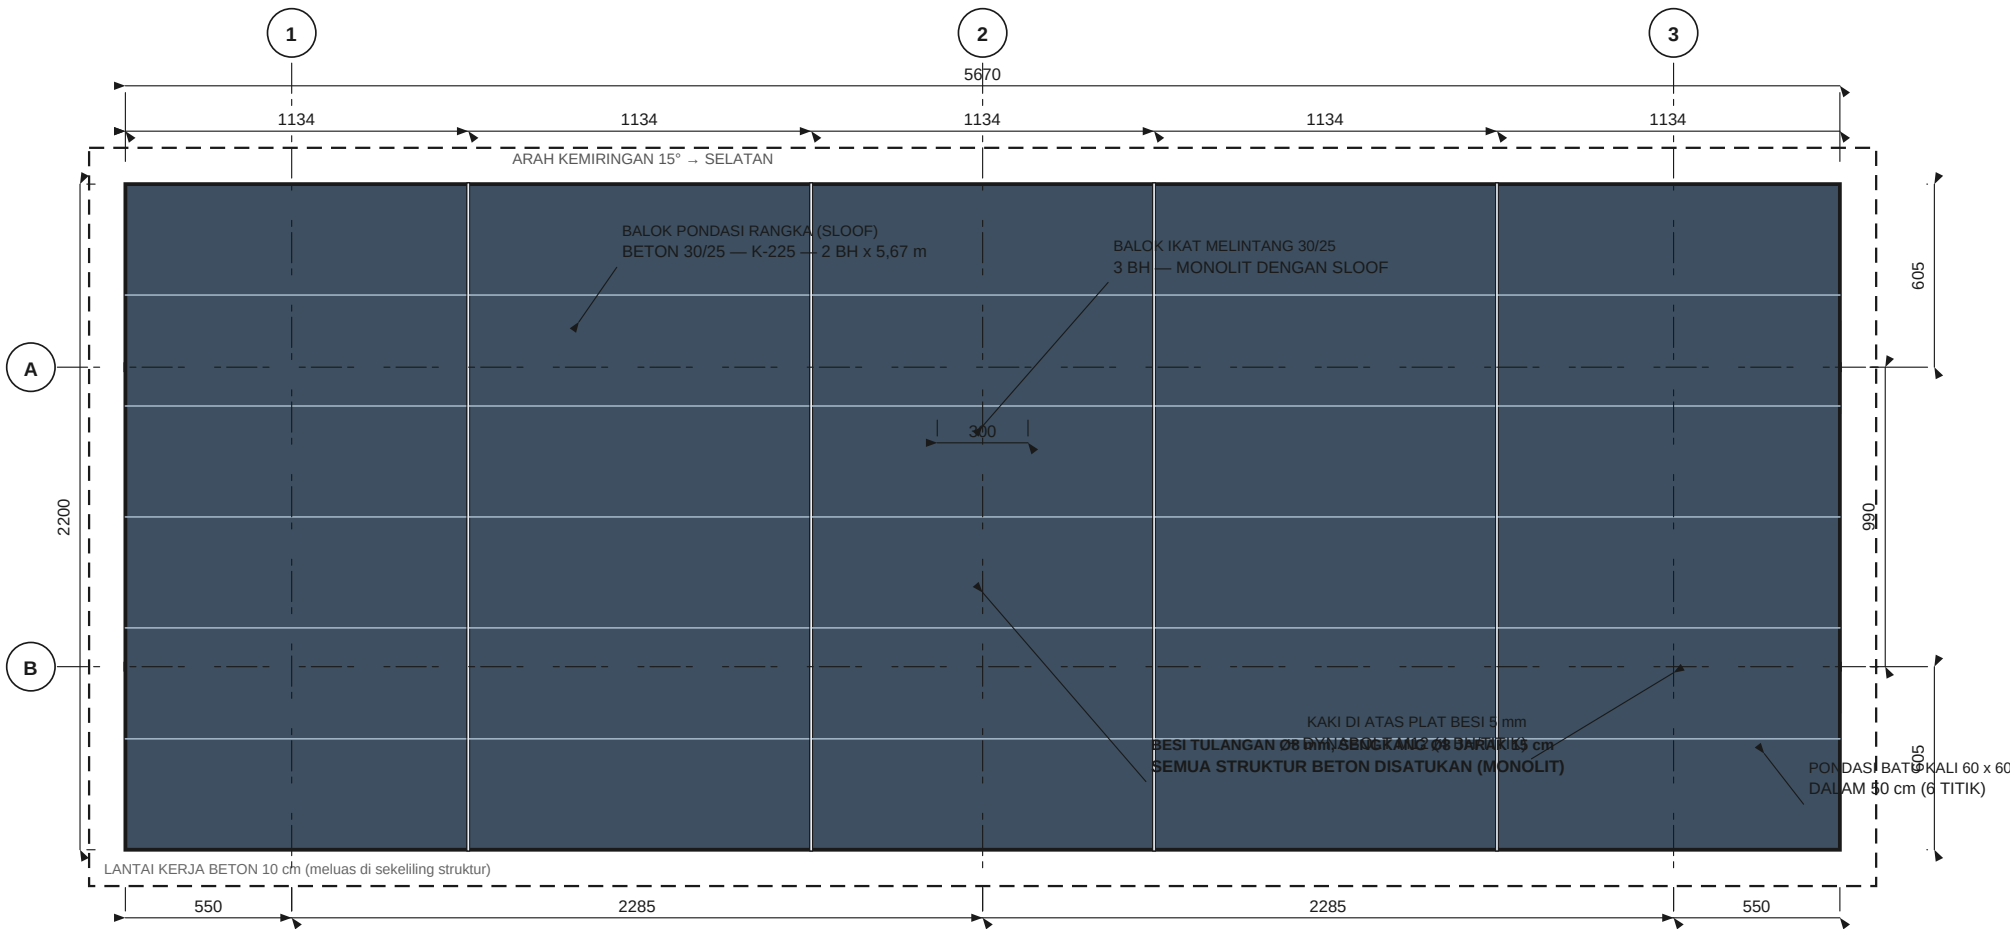

TAMPAK ATAS — RANGKA & BETON

SKALA 1 : 25

CATATAN :

- Semua ukuran dalam milimeter (mm), elevasi dalam meter dari ±0.00 lantai kerja. Gambar menyempurnakan draft awal; dimensi antar tampak telah diserasikan.
- Modul surya 550 Wp sebanyak 5 unit (total 2,75 kWp), dipasang portrait, kemiringan 15 derajat menghadap UTARA (sesuaikan azimuth dengan lokasi site).
- Rangka seluruhnya baja hollow galvanis 40 x 20 mm (tebal min. 1,6 mm). Semua sambungan rangka DILAS dan diperiksa kerataannya.
- Kaki rangka diangkur ke sloof melalui plat besi 5 mm (100 x 100 mm) dengan 4 dynabolt M12 per titik. Pastikan plat rata & level (toleransi ±5 mm).
- Sloof & balok ikat beton mutu K-225, tulangan Ø8 mm, besi cincin (senggang) jarak 15 cm. Semua struktur beton dituang monolit (disatukan).
- Pondasi batu kali 6 titik: lebar atas 30 cm, bawah 60 cm, kedalaman 50 cm di bawah sloof. Lantai kerja beton tebal 10 cm di sekeliling struktur.
- Jarak antar rangka (sumbu 1-2-3) 2285 mm; kantilever rail di ujung 550 mm. Rail memanjang 2 jalur di atas baris kaki.
- Pembumian (grounding) rangka & modul serta instalasi kabel DC mengikuti PUIL 2011 dan petunjuk pabrikan modul.


LEGENDA :

- Tepi benda terlihat
- Tepi benda tersembunyi
- Garis dimensi / leader
- Garis sumbu
- Arsir beton / detail tipis
- Kotak gelap : modul surya
- Tanah asli

DAFTAR LEMBAR GAMBAR :

G-01	TAMPAK ATAS
G-02	TAMPAK DEPAN
G-03	TAMPAK SAMPING (POTONGAN A-A)
G-04	TAMPAK ATAS - PANEL SURYA DISAMARKAN (RANGKA)
G-05	TAMPAK ATAS - PANEL DIHILANGKAN (RANGKA & BETON)
G-06	TAMPAK ATAS - PANEL & RANGKA DISAMARKAN (BETON)

DIGAMBAR	DIPERIKSA	DISAHKAN			
NAMA / TGL :	NAMA / TGL :	NAMA / TGL :			
PEMBANGUNAN PLTS GROUND MOUNT 2,75 kWp					
LOKASI / PEKERJAAN : (diisi sesuai lokasi proyek)					
JUDUL GAMBAR : TAMPAK ATAS — RANGKA PANEL & STRUKTUR BETON					
NO. GAMBAR	SKALA	SAT.	TANGGAL	REVISI	STATUS
G-05	1 : 25	mm	18-09-2026	0	KONSTRUKSI

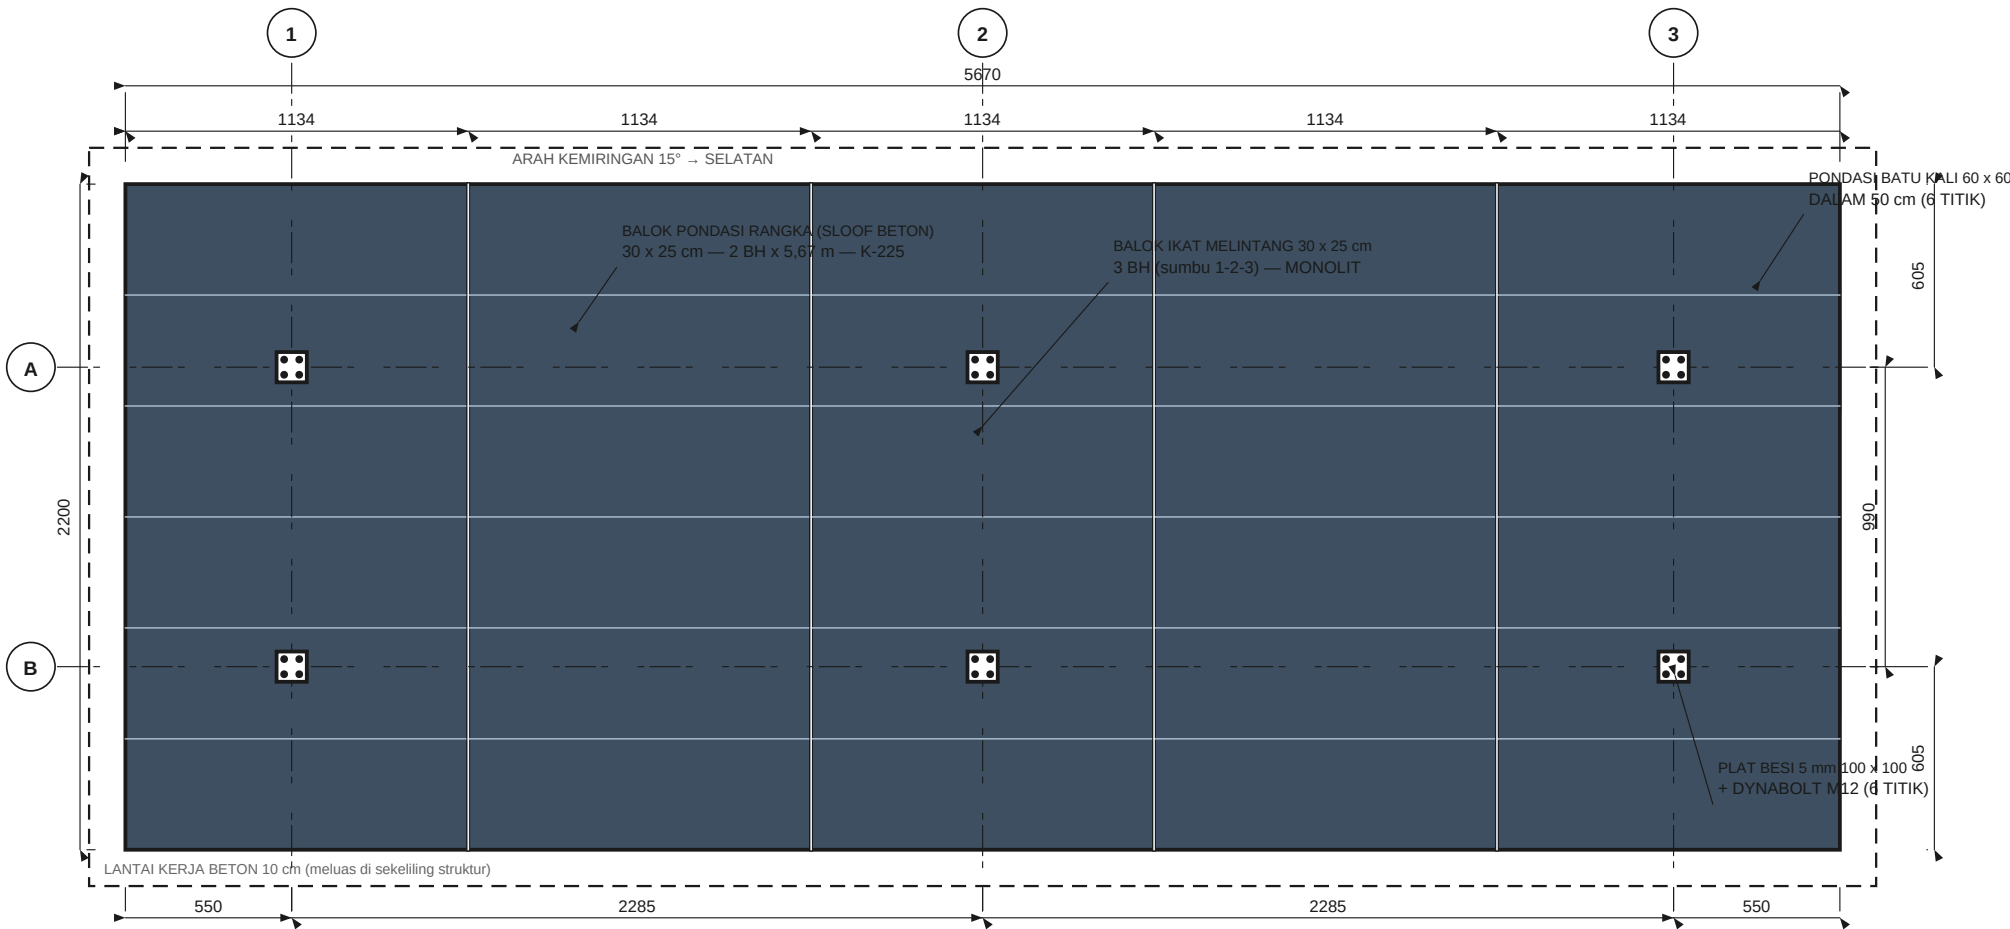

LEGENDA :

- Tepi benda terlihat
- Tepi benda tersembunyi
- Garis dimensi / leader
- Garis sumbu
- Arsir beton / detail tipis
- Kotak gelap : modul surya
- Tanah asli

DAFTAR LEMBAR GAMBAR :

G-01	TAMPAK ATAS
G-02	TAMPAK DEPAN
G-03	TAMPAK SAMPING (POTONGAN A-A)
G-04	TAMPAK ATAS - PANEL SURYA DISAMARKAN (RANGKA)
G-05	TAMPAK ATAS - PANEL DIHILANGKAN (RANGKA & BETON)
G-06	TAMPAK ATAS - PANEL & RANGKA DISAMARKAN (BETON)

TAMPAK ATAS — STRUKTUR BETON

SKALA 1 : 25

PLAT ANGKUR & SAMBUNGAN KAKI:

LIHAT DETAIL A PADA LEMBAR G-02 (SKALA 1 : 5)

Plat besi 5 mm 100 x 100 mm diangkur dengan 4 dynabolt M12 ke sloof pada 6 titik kaki rangka (sumbu 1-2-3, baris A-B).

CATATAN :

- Semua ukuran dalam milimeter (mm), elevasi dalam meter dari ±0.00 lantai kerja. Gambar menyempurnakan draft awal; dimensi antar tampak telah diserasikan.
- Modul surya 550 Wp sebanyak 5 unit (total 2,75 kWp), dipasang portrait, kemiringan 15 derajat menghadap UTARA (sesuaikan azimuth dengan lokasi site).
- Rangka seluruhnya baja hollow galvanis 40 x 20 mm (tebal min. 1,6 mm). Semua sambungan rangka DILAS dan diperiksa kerataannya.
- Kaki rangka diangkur ke sloof melalui plat besi 5 mm (100 x 100 mm) dengan 4 dynabolt M12 per titik. Pastikan plat rata & level (toleransi ±5 mm).
- Sloof & balok ikat beton mutu K-225, tulangan Ø8 mm, besi cincin (senggang) jarak 15 cm. Semua struktur beton dituang monolit (disatukan).
- Pondasi batu kali 6 titik: lebar atas 30 cm, bawah 60 cm, kedalaman 50 cm di bawah sloof. Lantai kerja beton tebal 10 cm di sekeliling struktur.
- Jarak antar rangka (sumbu 1-2-3) 2285 mm; kantilever rail di ujung 550 mm. Rail memanjang 2 jalur di atas baris kaki.
- Pembumian (grounding) rangka & modul serta instalasi kabel DC mengikuti PUIL 2011 dan petunjuk pabrikan modul.

DIGAMBAR		DIPERIKSA		DISAHKAN	
NAMA / TGL :		NAMA / TGL :		NAMA / TGL :	
PEMBANGUNAN PLTS GROUND MOUNT 2,75 kWp					
LOKASI / PEKERJAAN : (diisi sesuai lokasi proyek)					
JUDUL GAMBAR : TAMPAK ATAS — STRUKTUR BETON (PANEL & RANGKA DISAMARKAN)					
NO. GAMBAR	SKALA	SAT.	TANGGAL	REVISI	STATUS
G-06	1 : 25	mm	18-09-2026	0	KONSTRUKSI